

PROPOSED COMMERCIAL DEVELOPMENT

FOR


FROST

AT

CALL PACK ,TRADE FAIR ,LAGOS NIGERIA

JULY, 2022

ARCHITECTURAL DRAWING
(Main Building)

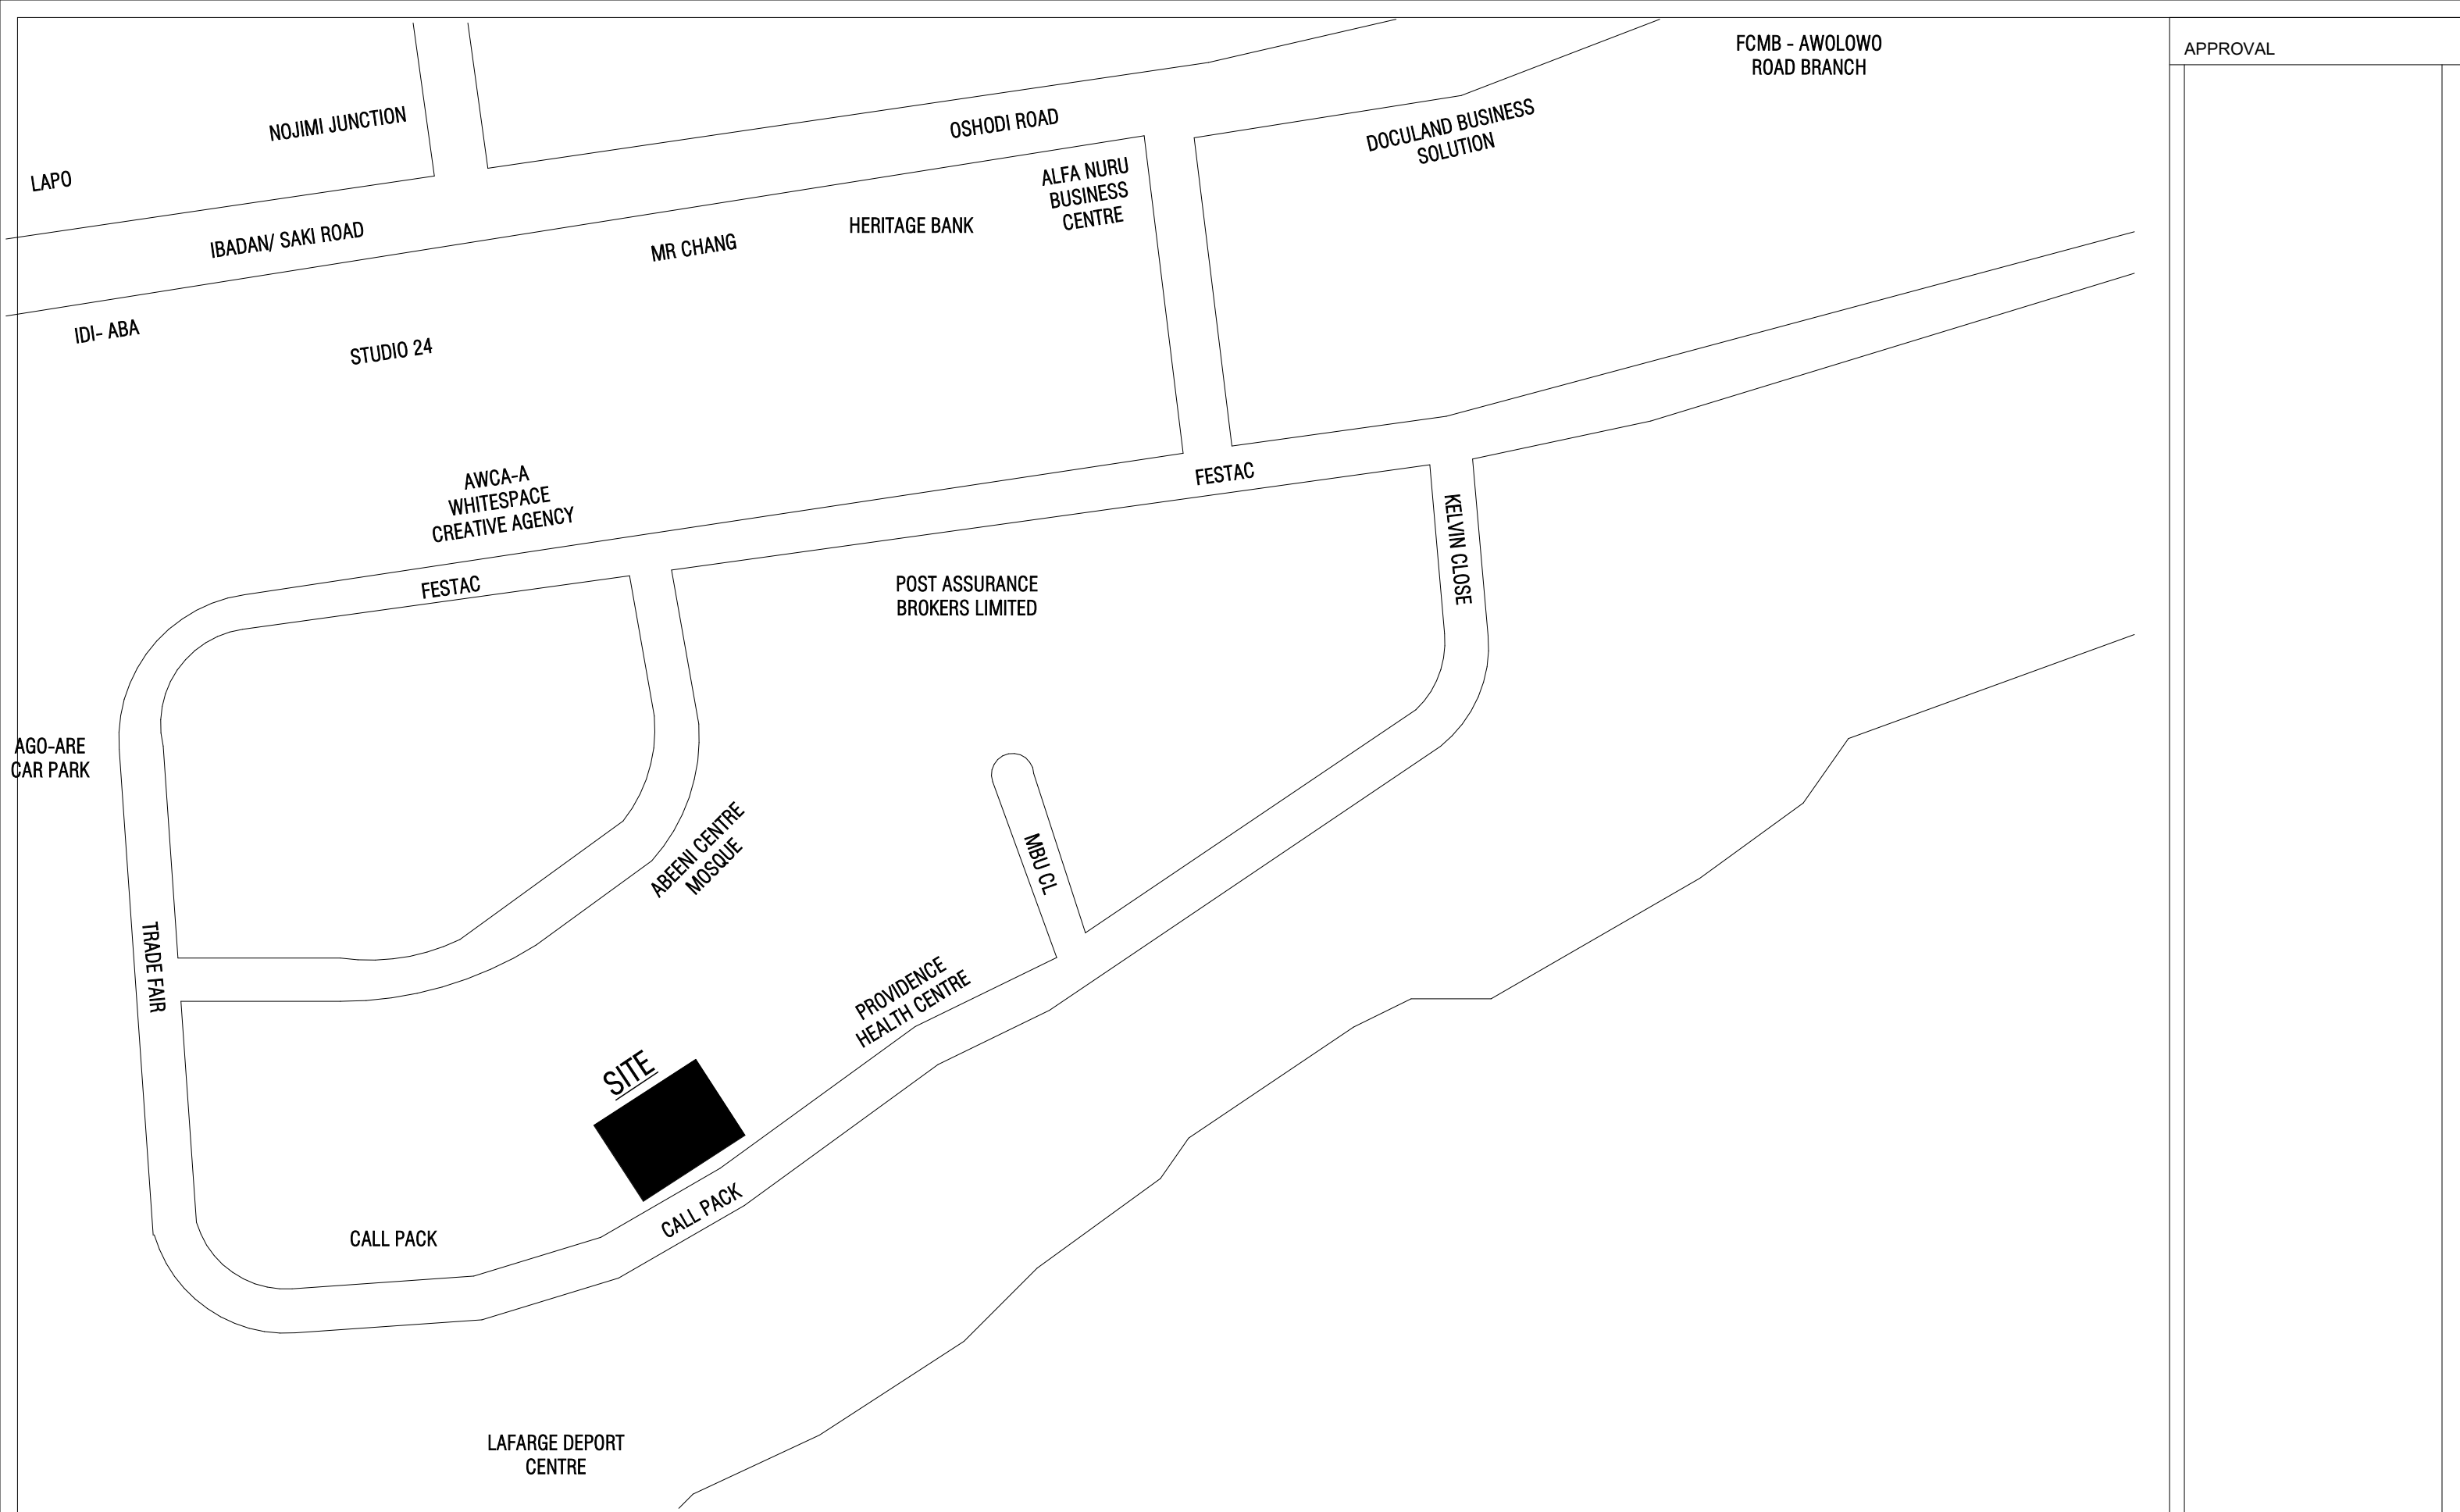

APPROVAL

NOTES:

- * All dimensions are in millimeters
- * All dimensions are to be verified on site
- * No dimension to be scaled from drawing
- * Architect to be notified of any discrepancy/changes & he alone will decide on the final instruction

CLIENT:

FROST

PROJECT NAME & ADDRESS.

PROPOSED COMMERCIAL DEVELOPMENT

AT CALL PACK, TRADE FAIR ,LAGOS , NIGERIA

DRAWING TITLE:

LOCATION MAP

DATE: JULY,2022

SCALE:

1 : 120

SHEET NO:

A103

FIRM NAME & ADDRESS:


PELICAN CONSTRUCTION

DRAWN BY:

OLALEKE

CHECKED BY:

ARC. OLALEKE

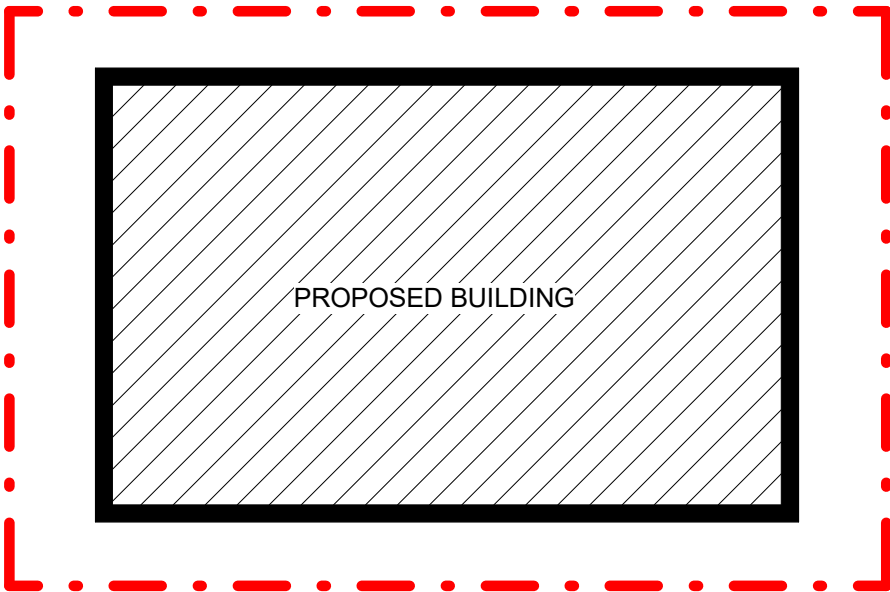

SITE ANALYSIS/ DETAILS

AREA OF SITE	87.326	SQ. MTRS
AREA OF MAIN BUILDING	55.616	SQ. MTRS
AREA OF BUILT SPACE	55.616	SQ. MTRS
AREA OF UNBUILT SPACE	31.710	SQ. MTRS
TOTAL LANDSCAPE/GREEN AREA	12.308	SQ. MTRS
% OF MAIN BUILDING	63.68%	
%OF UNBUILT AREA	36.32%	
% LANDSCAPE/GREEN AREA	10.90%	

SITE ANALYSIS/ DETAILS

TOTAL NOS OF UNIT	2
TOTAL NOs OF FLOORS	3
NO OF PARKING	5
TOTAL BUILDING AREA	315.324 SQ. MTRS

NOTE:

- A. REFERENCE LEVEL OF +000 TO BE ESTABLISHED ON SITE IN ACCORDANCE TO EXISTING SITE TOPOGRAPHY
- B. SPOT LEVELS ON THE DRAWINGS ARE INDICATIVE OF SPOT DIFFERENCES ONLY AND SHOULD BE SET OUT IN RELATION TO EXISTING SITE TOPOGRAPHY
- C. SITE REFERNCES OF +000 **MUST** BE AT LEAST 150MM HIGHER THAN THE EXISTING ROAD

GENERAL NOTES

1. KERBS-100X450mm TOP EDGED BEVELLED CONC. KERB TO S/ENGR'S DETAILS
2. CAR PARK AND DRIVEWAY CONC. INTERLOCKING PAVING STONES ON SAND BED TO S/ENGR'S dETAILS EXCEPT OTHERWISE STATED
3. GARDEN WALKWAY-STAMPED CONCRETE FLOOR FINISH OF 1000X1000MM SLABS TO SPECIALIST dETAILS
4. GREEN-TOPSOIL AND GRASS TYPE AS SPECIFIED BY SPECIALIST
5. CAR PARK MARKING-ENAMEL PAINT OF APPROVED COLOUR
6. ALL EXTERNAL WORKS DRAWINGS PROVIDED BY OTHER CONCLTANTS MUST SHOW LOCATIONS,DETAILS AND SPECIFICATIONS OF ALL EXTERNAL FEATURES-LIGHT FITTINGS,MANHOLES ETC
7. ALL EXTERNAL WORKS DRAWINGS PROVIDED BY OTHER CONSULTANTS MUST BE READ IN CONJUNCTION WITH THIS SITE PLAN

NOTES:

- * All dimensions are in millimeters
- * All dimensions are to be verified on site
- * No dimension to be scaled from drawing
- * Architect to be notified of any discrepancy/changes & he alone will decide on the final instruction

CLIENT:

FROST

PROJECT NAME & ADDRESS.

PROPOSED COMMERCIAL DEVELOPMENT

AT CALL PACK, TRADE FAIR ,LAGOS , NIGERIA

DRAWING TITLE:

SITE PLAN

DATE:

JULY,2022

SCALE:

1 : 100

SHEET NO:

A104

FIRM NAME & ADDRESS:


PELICAN CONSTRUCTION

DRAWN BY:

OLALEKE

CHECKED BY:

ARC. OLALEKE

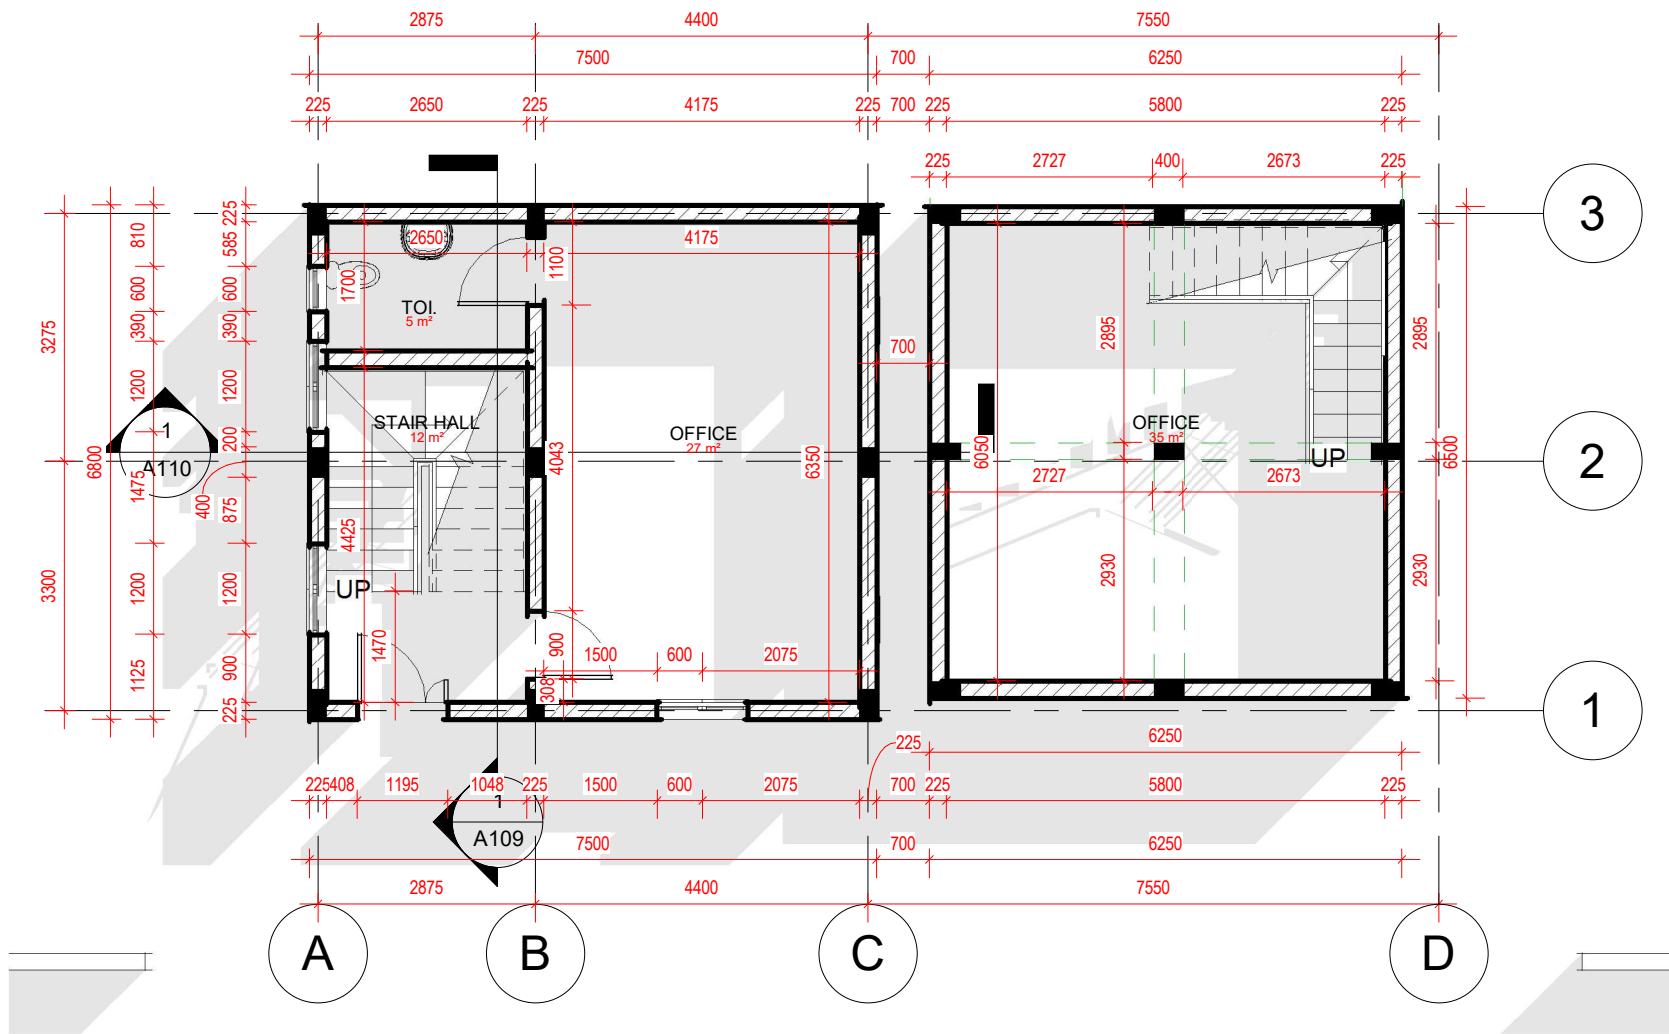

NOTES:

- * All dimensions are in millimeters
- * All dimensions are to be verified on site
- * No dimension to be scaled from drawing
- * Architect to be notified of any discrepancy/changes & he alone will decide on the final instruction

CLIENT:

FROST

PROJECT NAME & ADDRESS.

PROPOSED COMMERCIAL DEVELOPMENT
AT CALL PACK, TRADE FAIR ,LAGOS , NIGERIA

DRAWING TITLE:

GROUND FL

DATE: **JULY,2022**

SCALE:

1 : 100

SHEET NO:

A105

FIRM NAME & ADDRESS:


PELICAN CONSTRUCTION

DRAWN BY:

OLALEKE

CHECKED BY:

ARC. OLALEKE

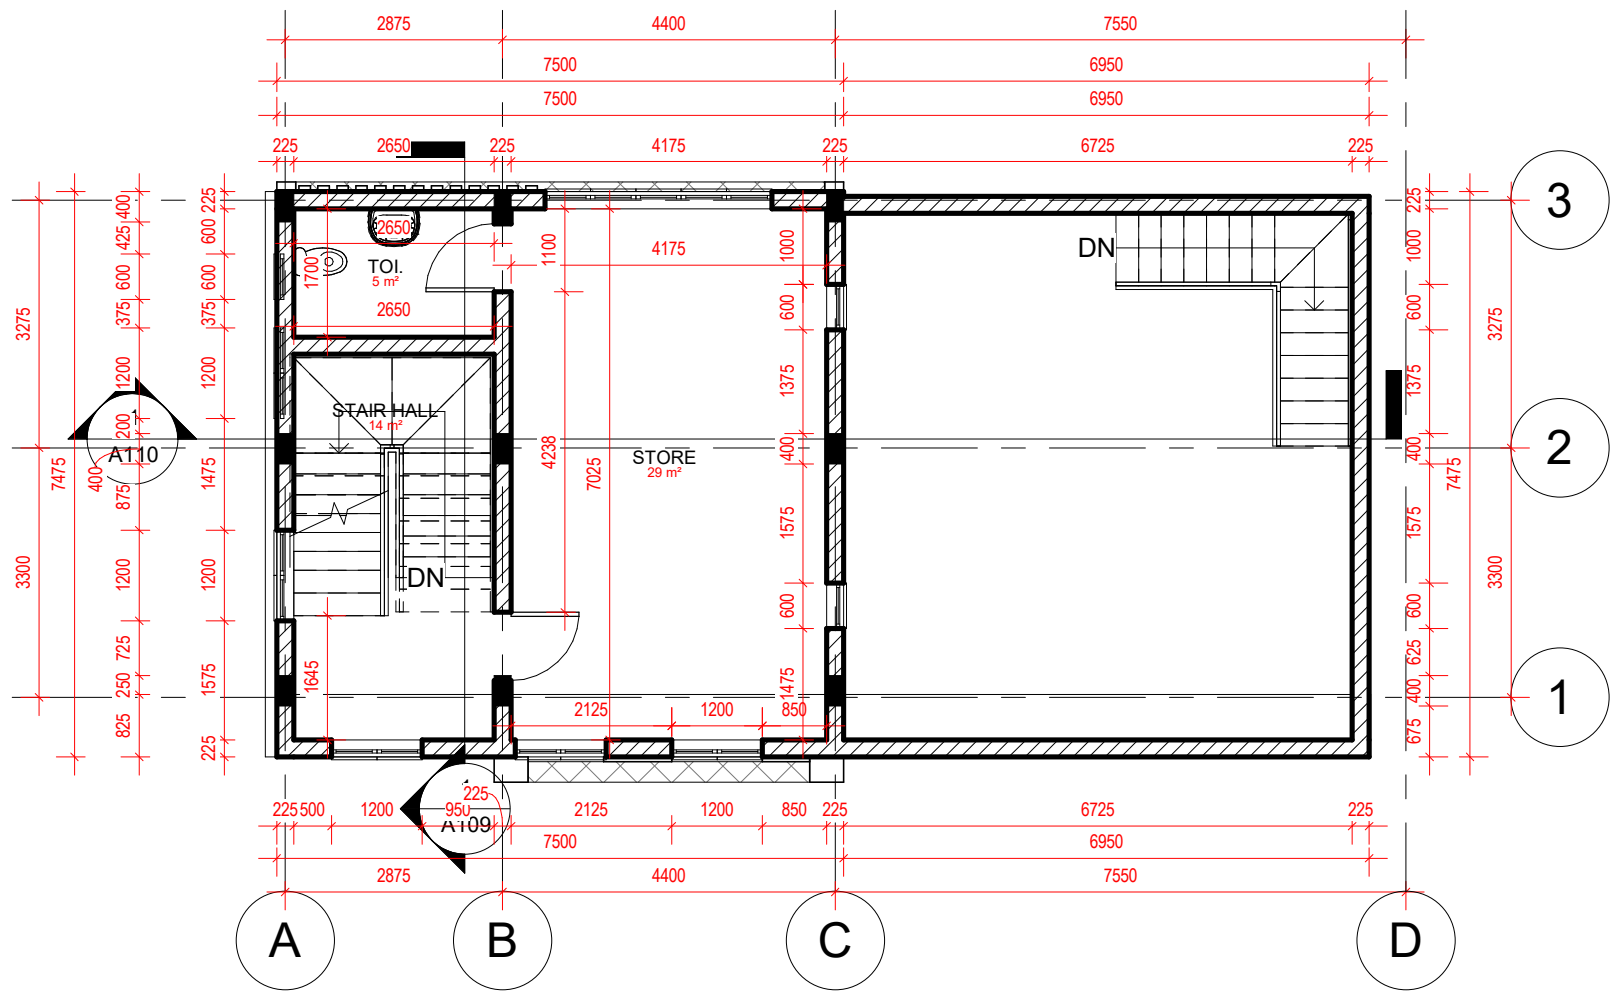

NOTES:

- * All dimensions are in millimeters
- * All dimensions are to be verified on site
- * No dimension to be scaled from drawing
- * Architect to be notified of any discrepancy/changes & he alone will decide on the final instruction

CLIENT:

FROST

PROJECT NAME & ADDRESS.

PROPOSED COMMERCIAL DEVELOPMENT

AT CALL PACK, TRADE FAIR ,LAGOS , NIGERIA

DRAWING TITLE:

TYPICAL FIRST
FLOOR L- SECOND
FLOOR L

DATE: JULY,2022

SCALE:

1 : 100

SHEET NO:

A106

FIRM NAME & ADDRESS:


PELICAN CONSTRUCTION

DRAWN BY:

OLALEKE

CHECKED BY:

ARC. OLALEKE

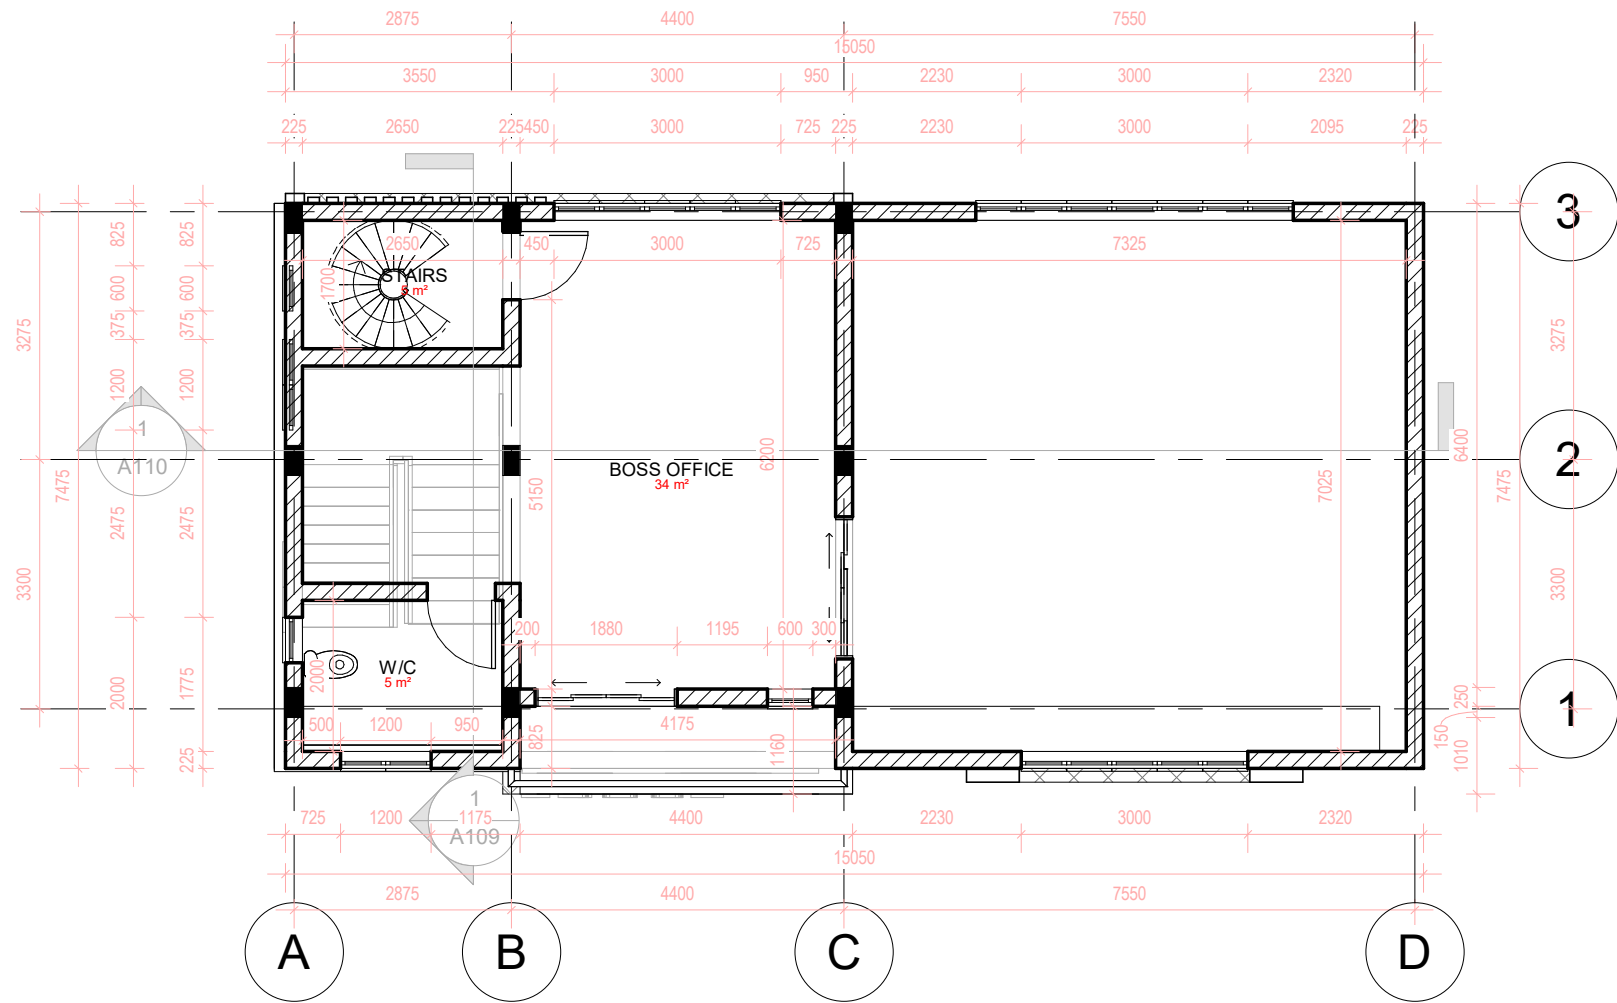

NOTES:

- * All dimensions are in millimeters
- * All dimensions are to be verified on site
- * No dimension to be scaled from drawing
- * Architect to be notified of any discrepancy/changes & he alone will decide on the final instruction

CLIENT:

FROST

PROJECT NAME & ADDRESS:

PROPOSED COMMERCIAL DEVELOPMENT

AT CALL PACK, TRADE FAIR ,LAGOS , NIGERIA

DRAWING TITLE:

PENT FLOOR

DATE: JULY,2022

SCALE:

1 : 100

SHEET NO:

A107

FIRM NAME & ADDRESS:


PELICAN CONSTRUCTION

DRAWN BY:

OLALEKE

CHECKED BY:

ARC. OLALEKE

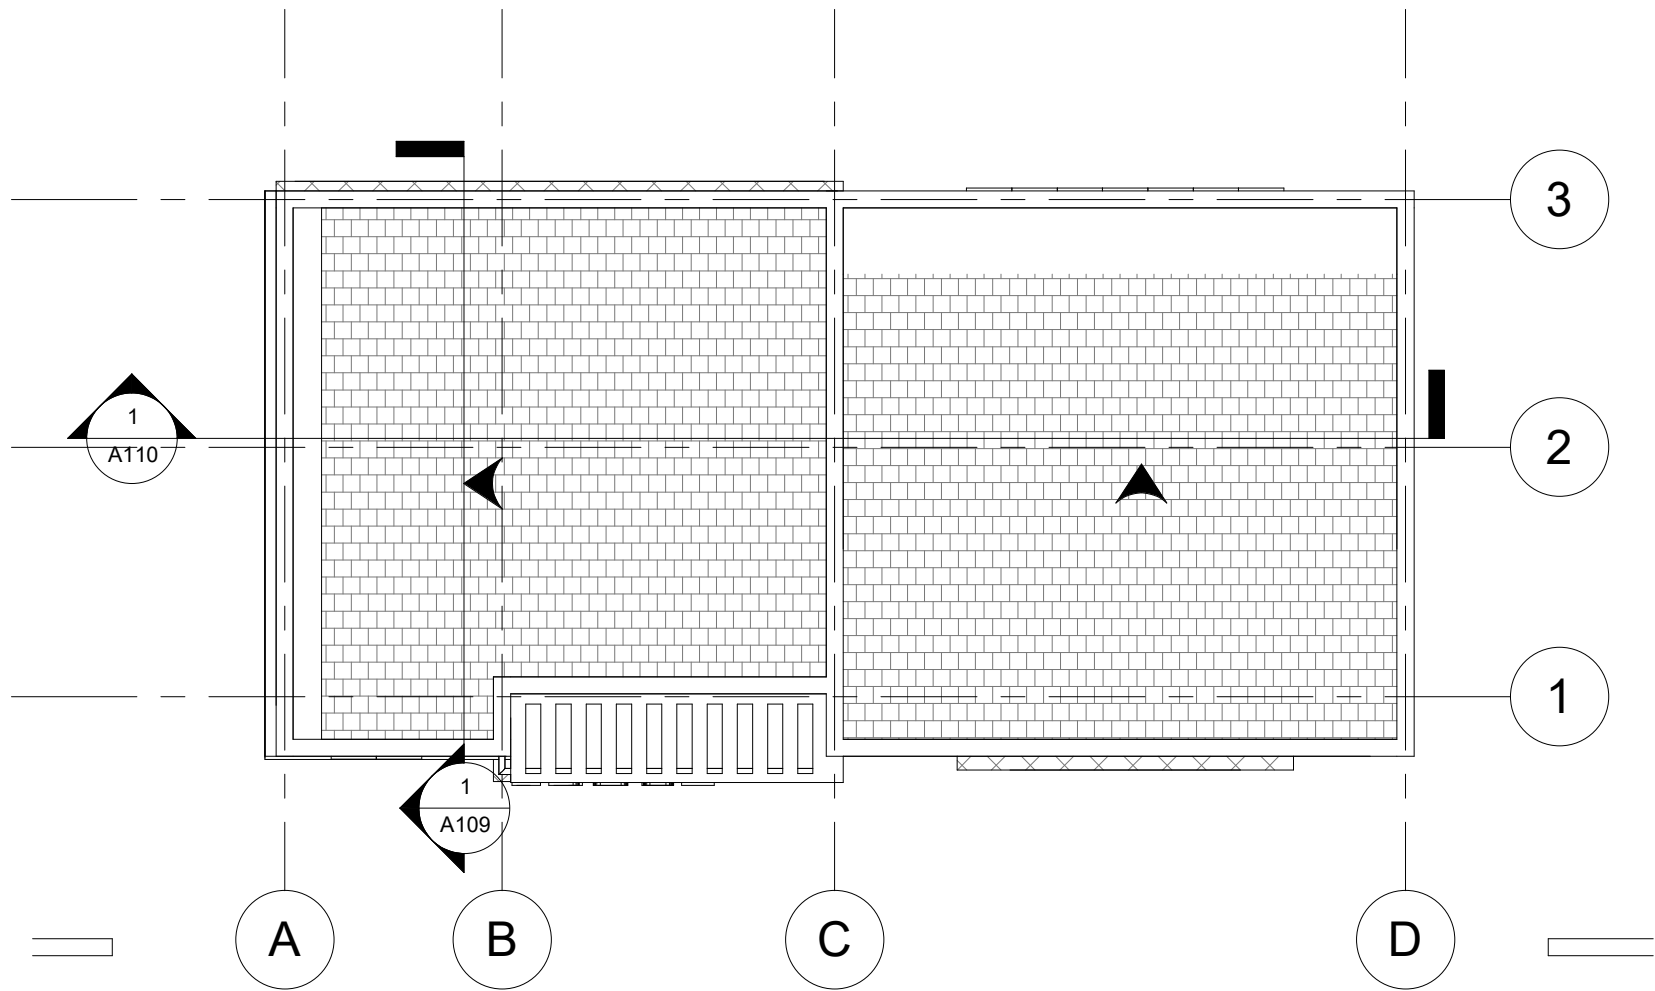

NOTES:

- * All dimensions are in millimeters
- * All dimensions are to be verified on site
- * No dimension to be scaled from drawing
- * Architect to be notified of any discrepancy/changes & he alone will decide on the final instruction

CLIENT:

FROST

PROJECT NAME & ADDRESS:

PROPOSED COMMERCIAL DEVELOPMENT

AT CALL PACK, TRADE FAIR ,LAGOS , NIGERIA

DRAWING TITLE:

ROOF PLAN

DATE:

JULY,2022

SCALE:

1 : 100

SHEET NO:

A108

FIRM NAME & ADDRESS:


PELICAN CONSTRUCTION

DRAWN BY:

OLALEKE

CHECKED BY:

ARC. OLALEKE

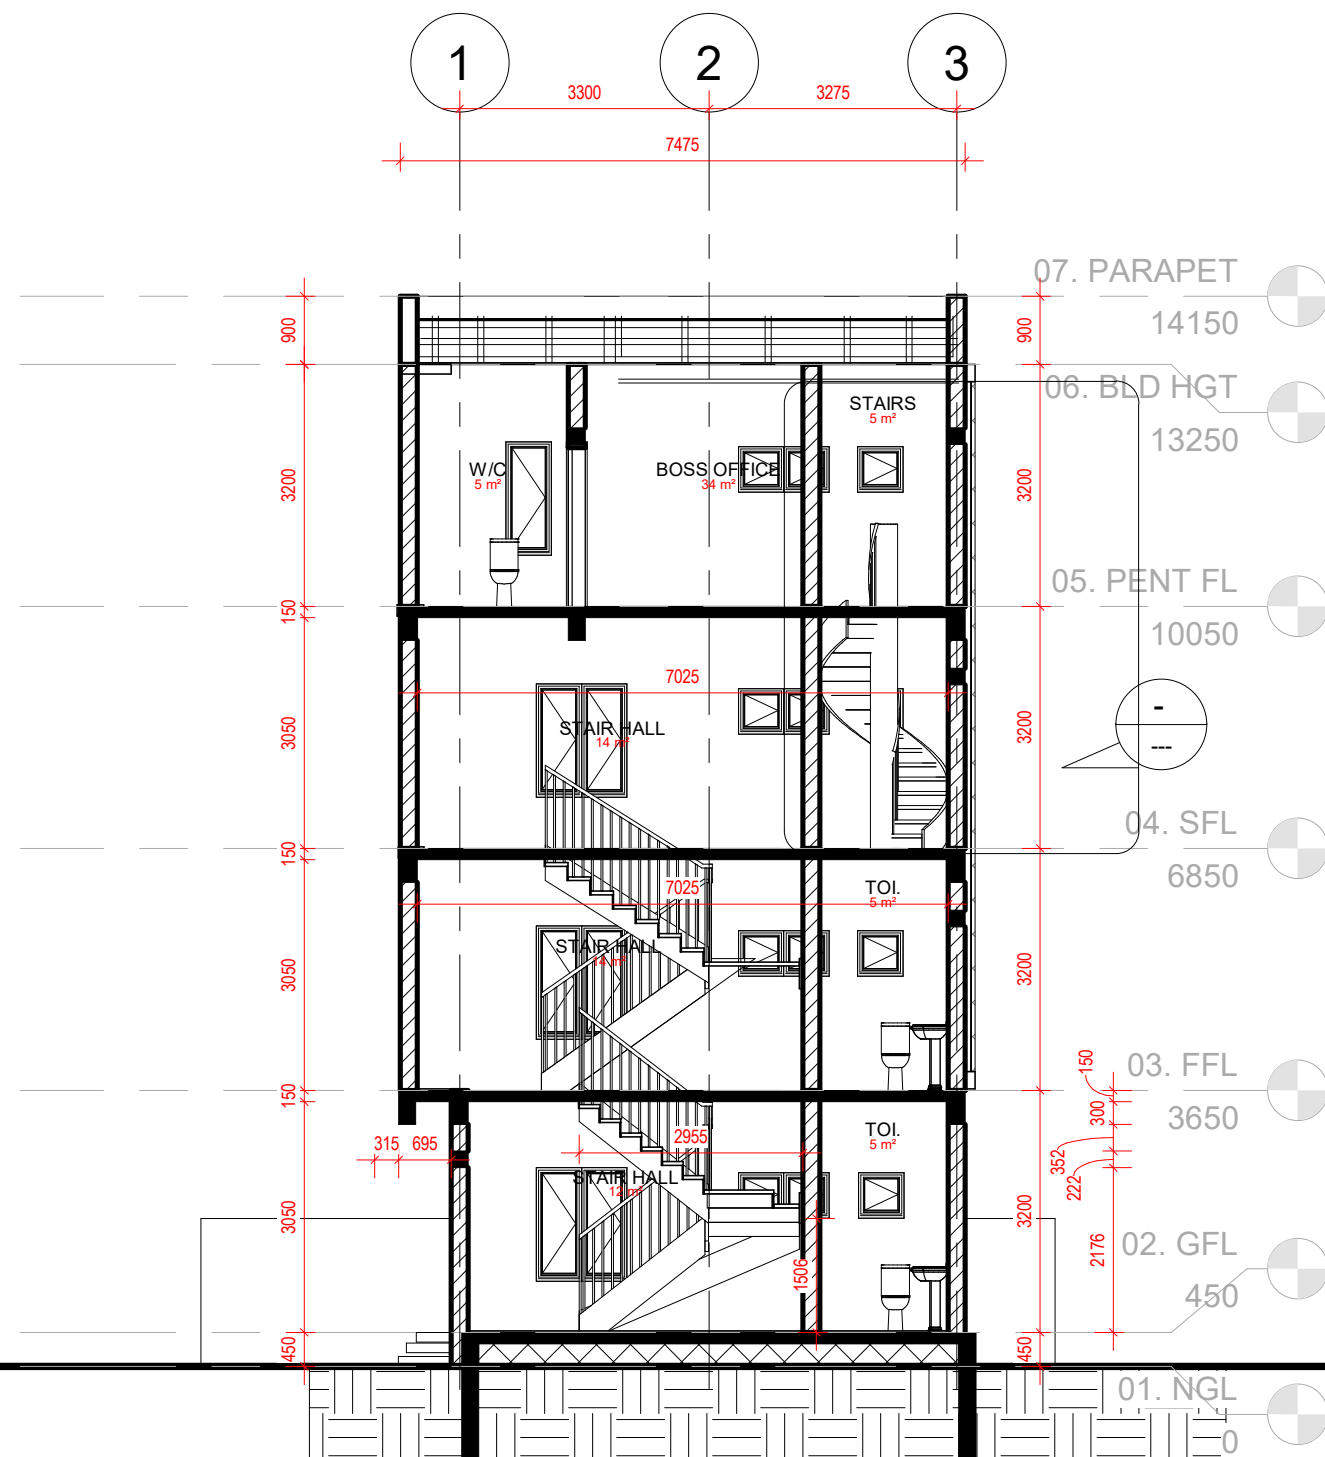

NOTES:

- * All dimensions are in millimeters
- * All dimensions are to be verified on site
- * No dimension to be scaled from drawing
- * Architect to be notified of any discrepancy/changes & he alone will decide on the final instruction

CLIENT:

FROST

PROJECT NAME & ADDRESS:

PROPOSED COMMERCIAL DEVELOPMENT

AT CALL PACK, TRADE FAIR ,LAGOS , NIGERIA

DRAWING TITLE:

CROSS SECTION

DATE: JULY,2022

SCALE:

1 : 100

SHEET NO:

A109

FIRM NAME & ADDRESS:


PELICAN CONSTRUCTION

DRAWN BY:

OLALEKE

CHECKED BY:

ARC. OLALEKE

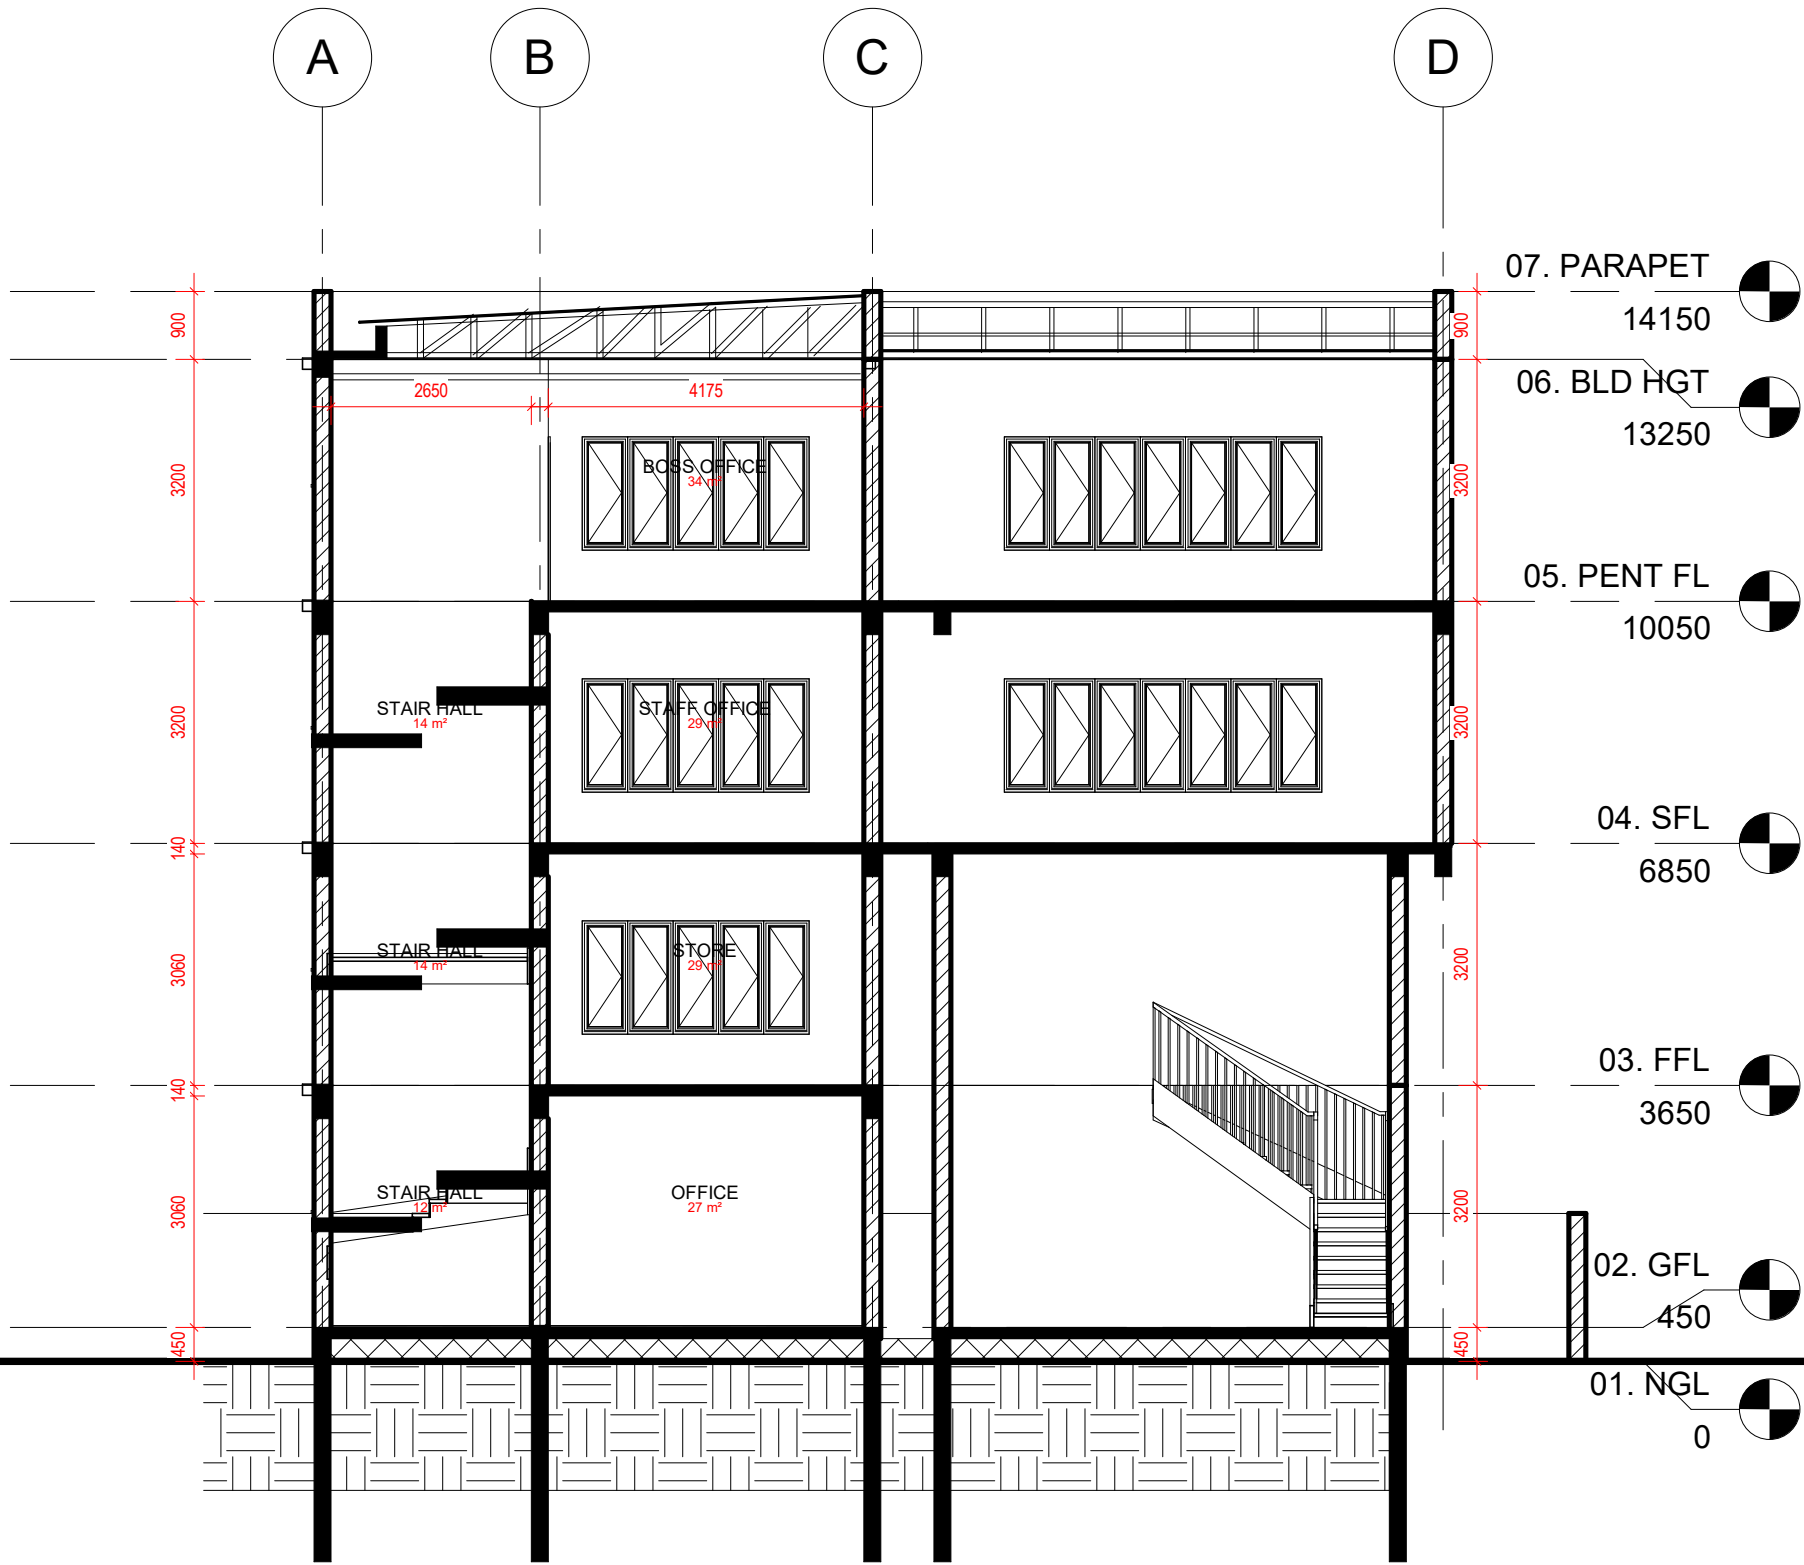

NOTES:

- * All dimensions are in millimeters
- * All dimensions are to be verified on site
- * No dimension to be scaled from drawing
- * Architect to be notified of any discrepancy/changes & he alone will decide on the final instruction

CLIENT:

FROST

PROJECT NAME & ADDRESS.

PROPOSED COMMERCIAL DEVELOPMENT

AT CALL PACK, TRADE FAIR ,LAGOS , NIGERIA

DRAWING TITLE:

LONGITUDINAL
SECTION

DATE: JULY,2022

SCALE:

1 : 100

SHEET NO:

A110

FIRM NAME & ADDRESS:


PELICAN CONSTRUCTION

DRAWN BY:

OLALEKE

CHECKED BY:

ARC. OLALEKE

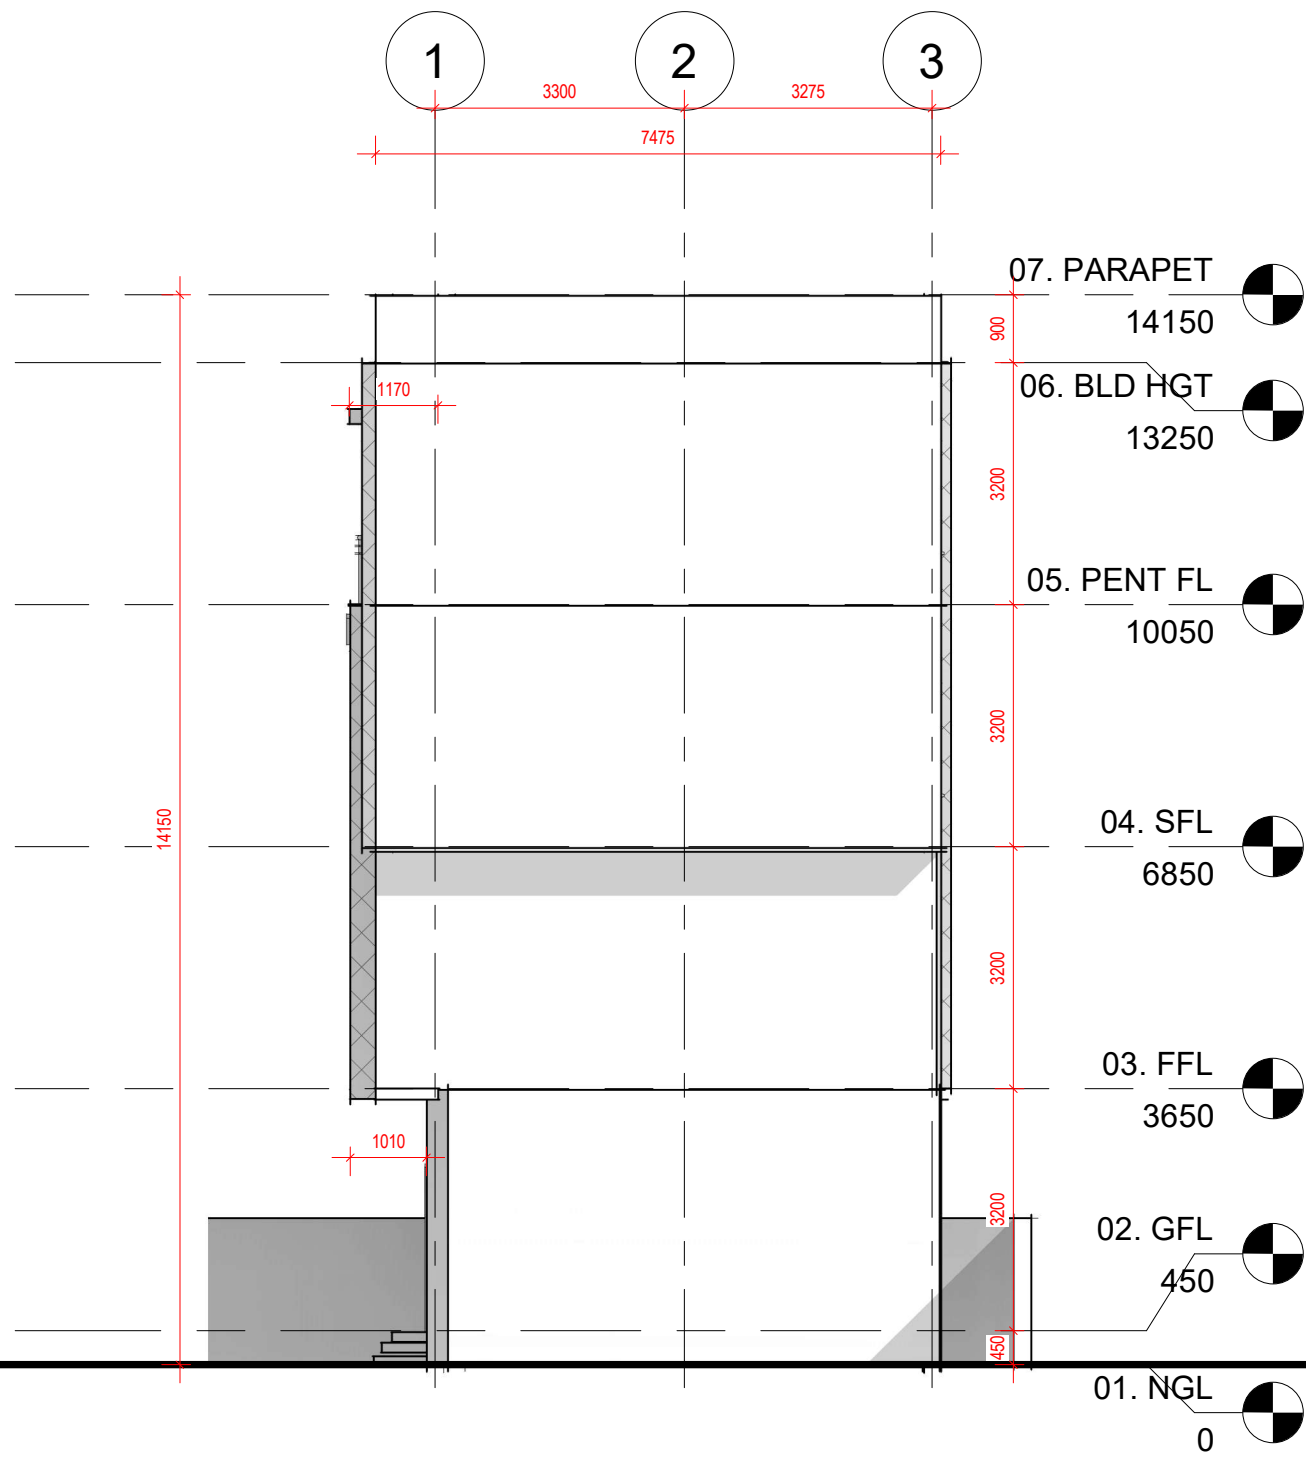

RIGHT SIDE VIEW

NOTES:

- * All dimensions are in millimeters
- * All dimensions are to be verified on site
- * No dimension to be scaled from drawing
- * Architect to be notified of any discrepancy/changes & he alone will decide on the final instruction

CLIENT:

FROST

PROJECT NAME & ADDRESS.

PROPOSED COMMERCIAL DEVELOPMENT

AT CALL PACK, TRADE FAIR ,LAGOS , NIGERIA

DRAWING TITLE:

ELEVATION

DATE: **JULY,2022**

SCALE:

1 : 100

SHEET NO:

A111

FIRM NAME & ADDRESS:


PELICAN CONSTRUCTION

DRAWN BY:

OLALEKE

CHECKED BY:

ARC. OLALEKE

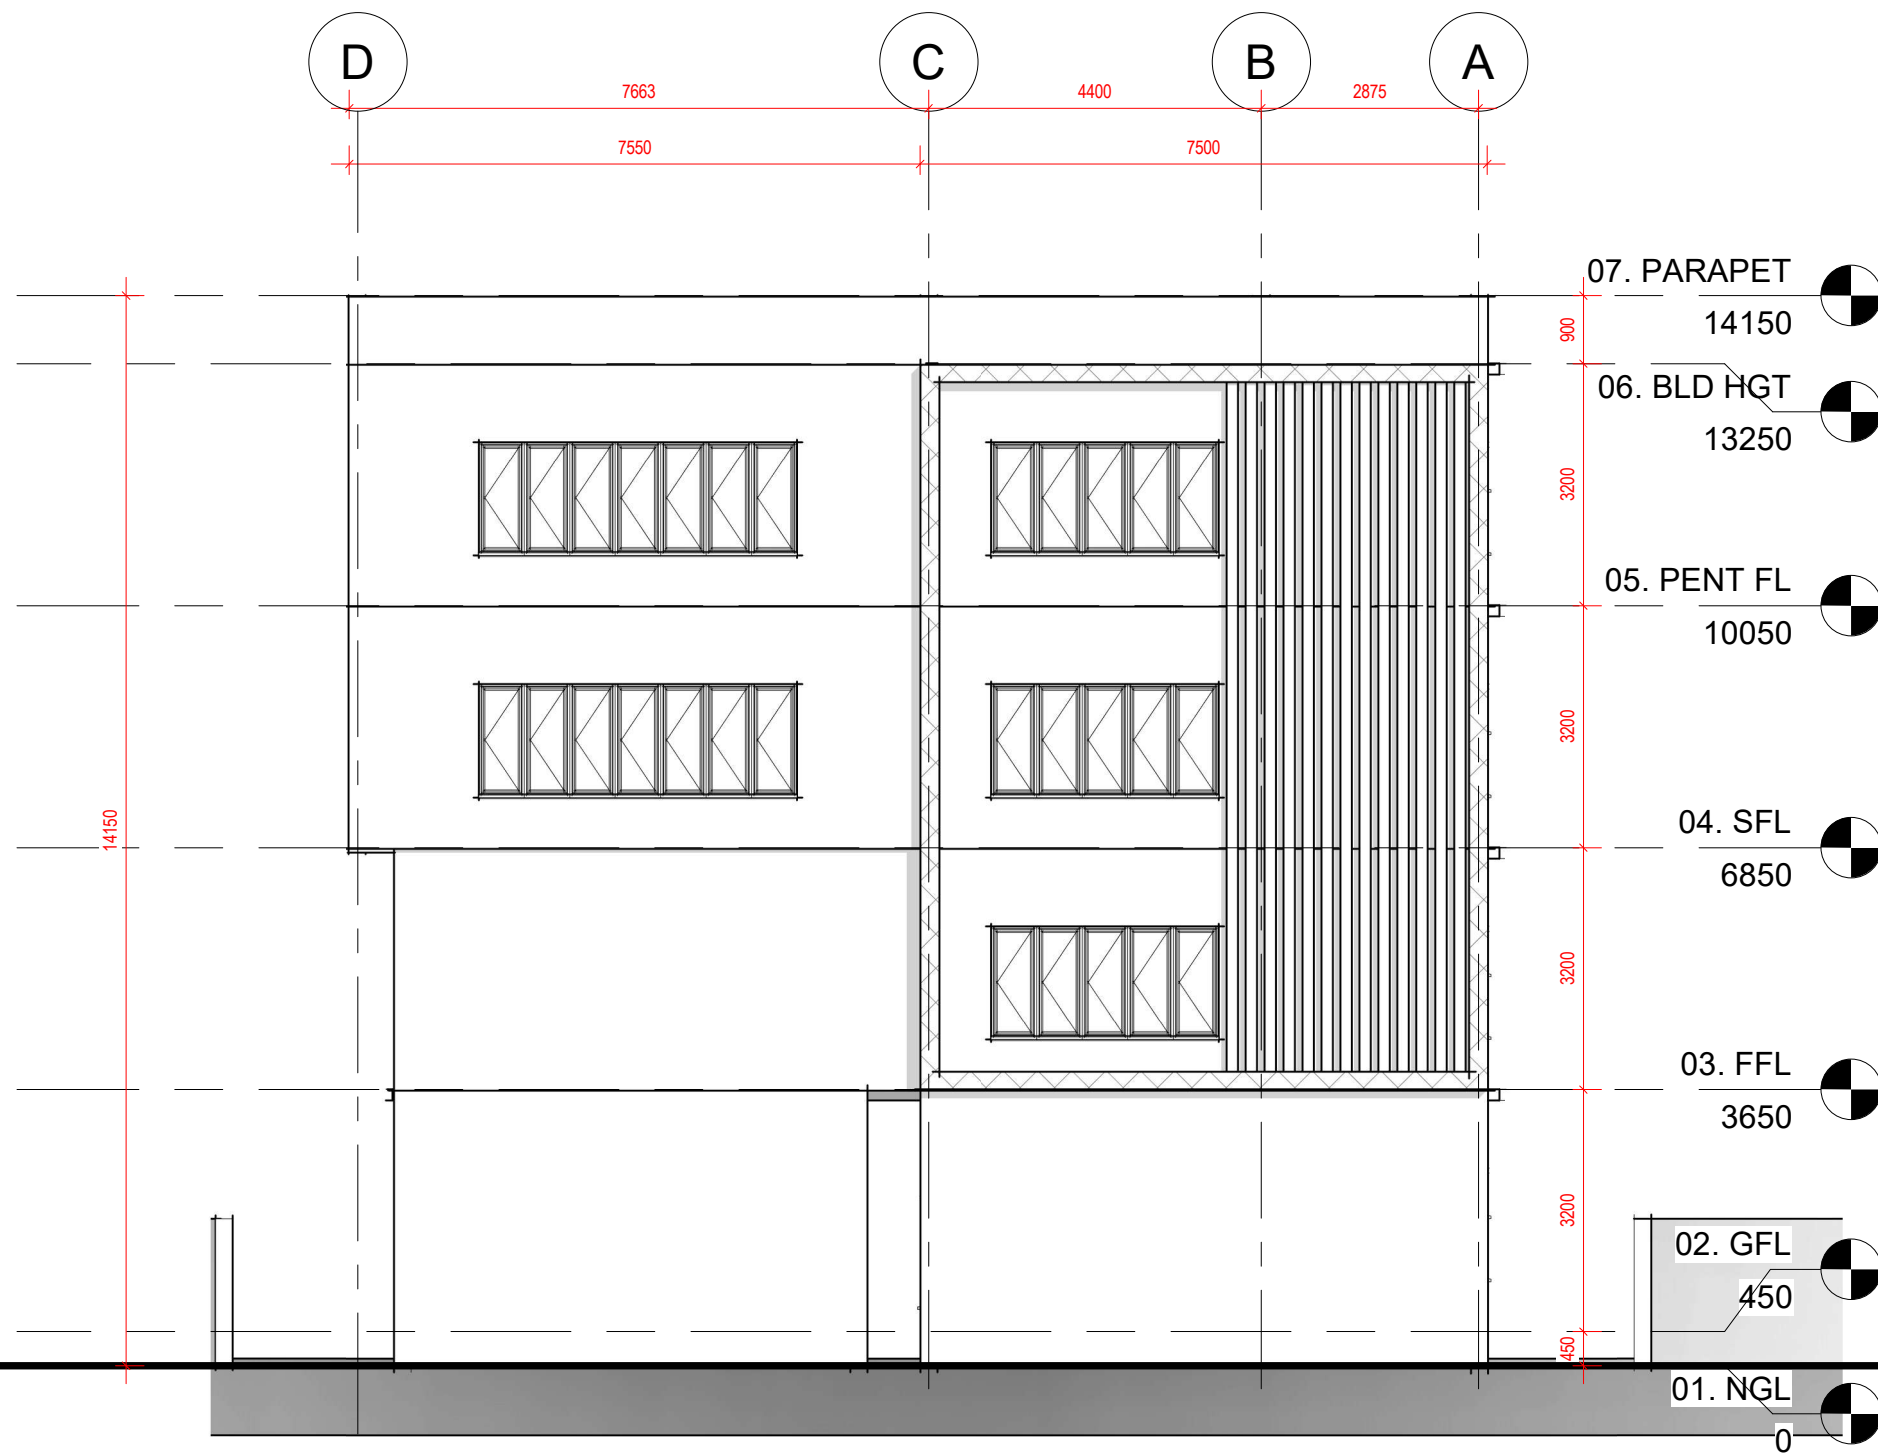

LEFT SIDE VIEW

NOTES:

- * All dimensions are in millimeters
- * All dimensions are to be verified on site
- * No dimension to be scaled from drawing
- * Architect to be notified of any discrepancy/changes & he alone will decide on the final instruction

CLIENT:

FROST

PROJECT NAME & ADDRESS:

PROPOSED COMMERCIAL DEVELOPMENT

AT CALL PACK, TRADE FAIR ,LAGOS , NIGERIA

DRAWING TITLE:

ELEVATION

DATE: JULY,2022

SCALE:

1 : 100

SHEET NO:

A112

FIRM NAME & ADDRESS:


PELICAN CONSTRUCTION

DRAWN BY:

OLALEKE

CHECKED BY:

ARC. OLALEKE

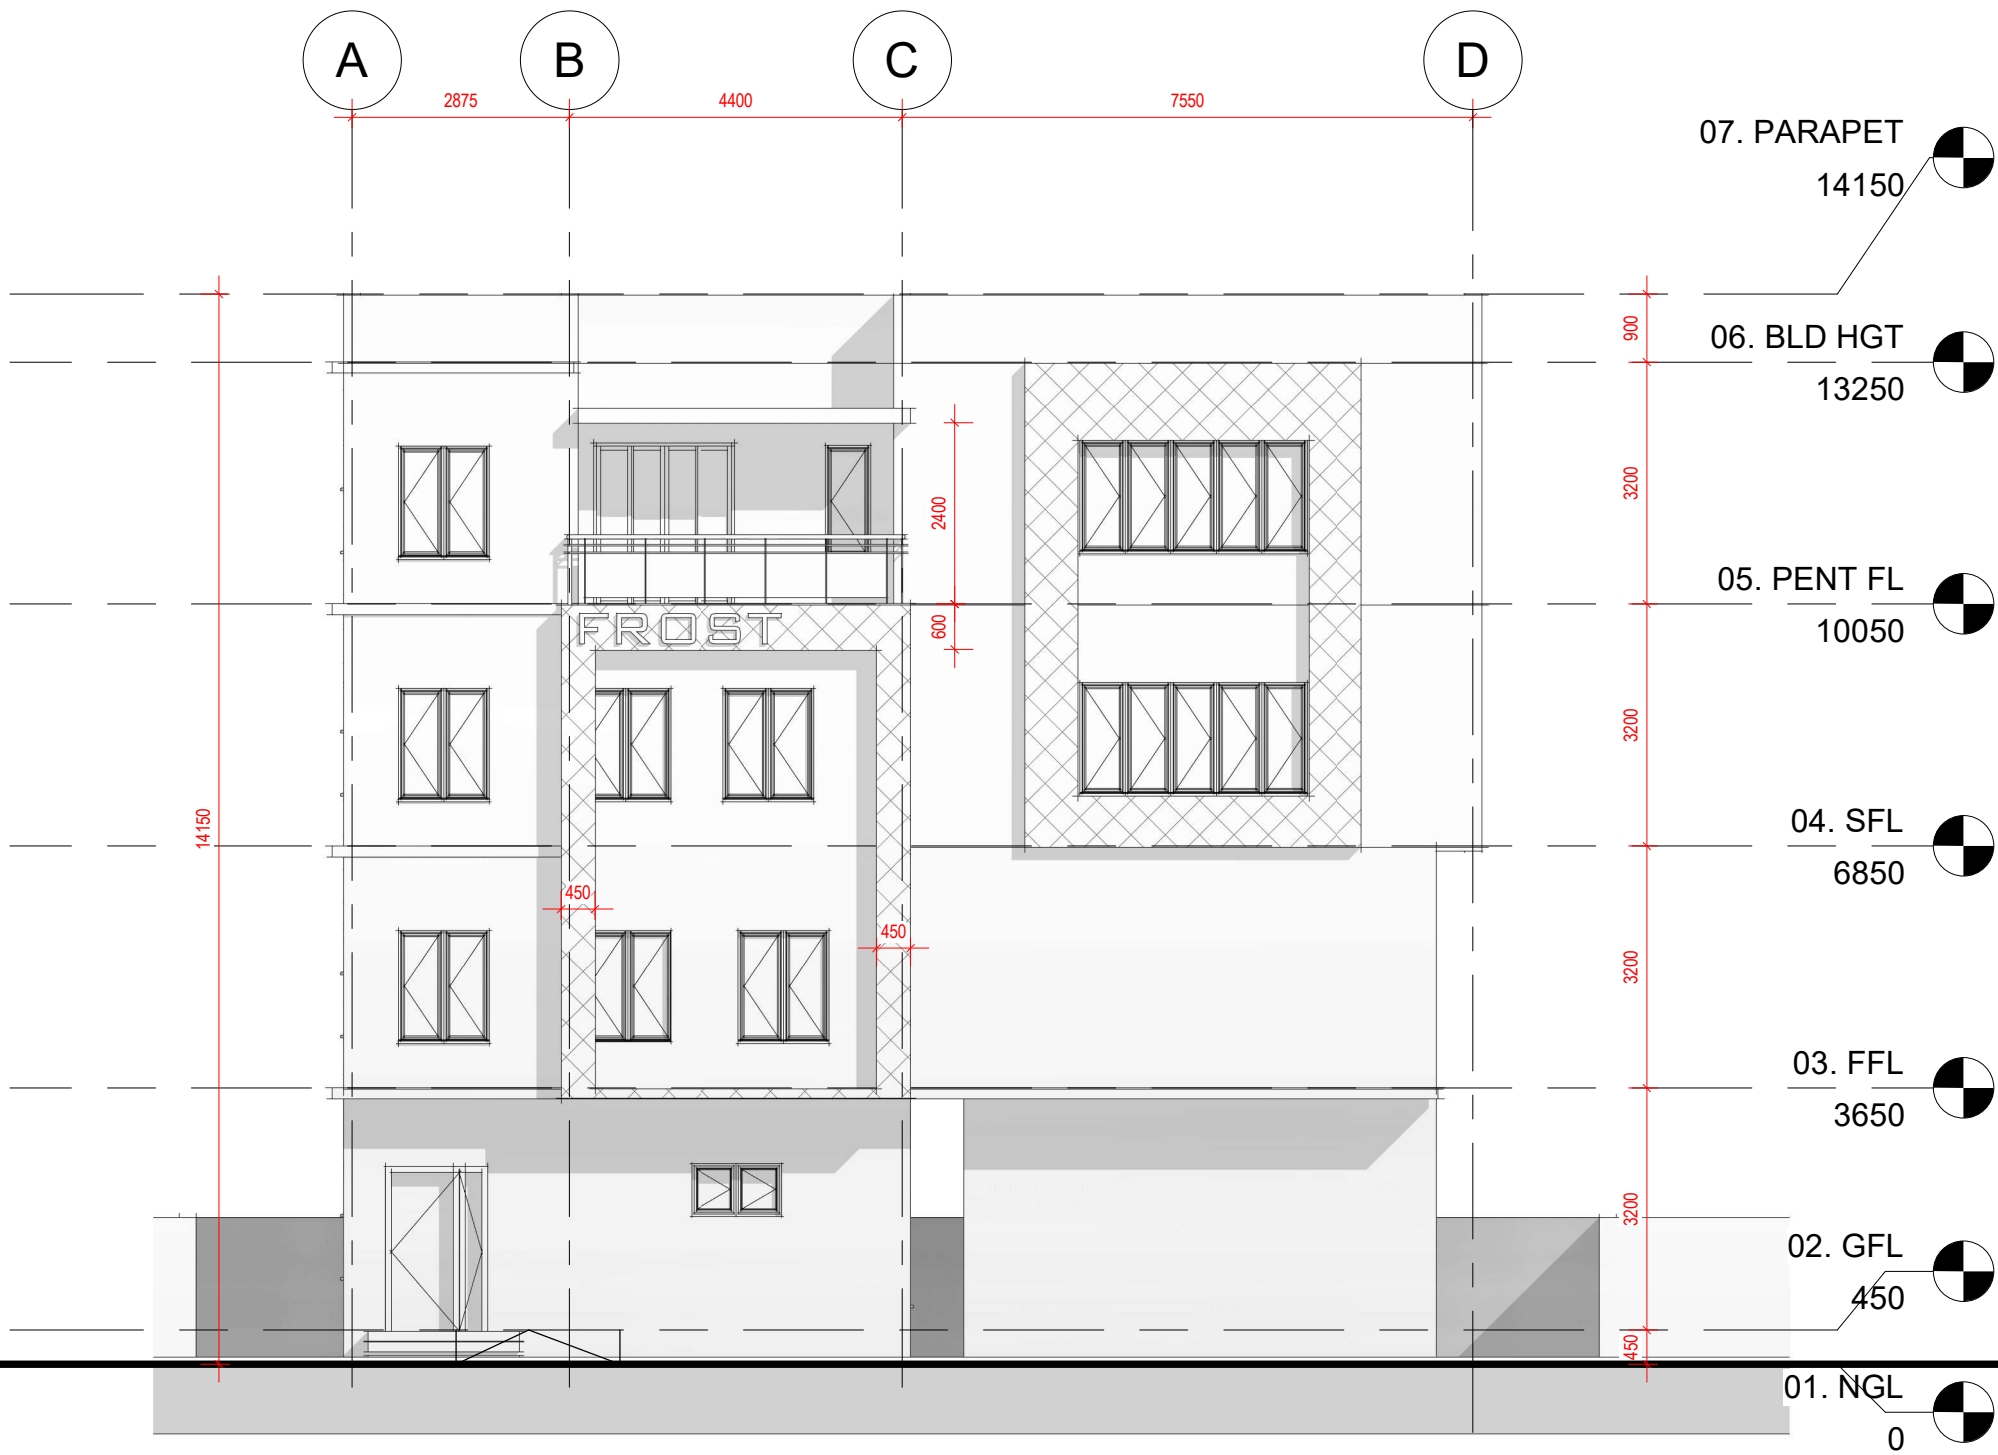

APPROACH VIEW

NOTES:

- * All dimensions are in millimeters
- * All dimensions are to be verified on site
- * No dimension to be scaled from drawing
- * Architect to be notified of any discrepancy/changes & he alone will decide on the final instruction

CLIENT:

FROST

PROJECT NAME & ADDRESS.

PROPOSED COMMERCIAL DEVELOPMENT
AT CALL PACK, TRADE FAIR ,LAGOS , NIGERIA

DRAWING TITLE:

ELEVATION

DATE: **JULY,2022**

SCALE:

1 : 100

SHEET NO:

A113

FIRM NAME & ADDRESS:


PELICAN CONSTRUCTION

DRAWN BY:

OLALEKE

CHECKED BY:

ARC. OLALEKE

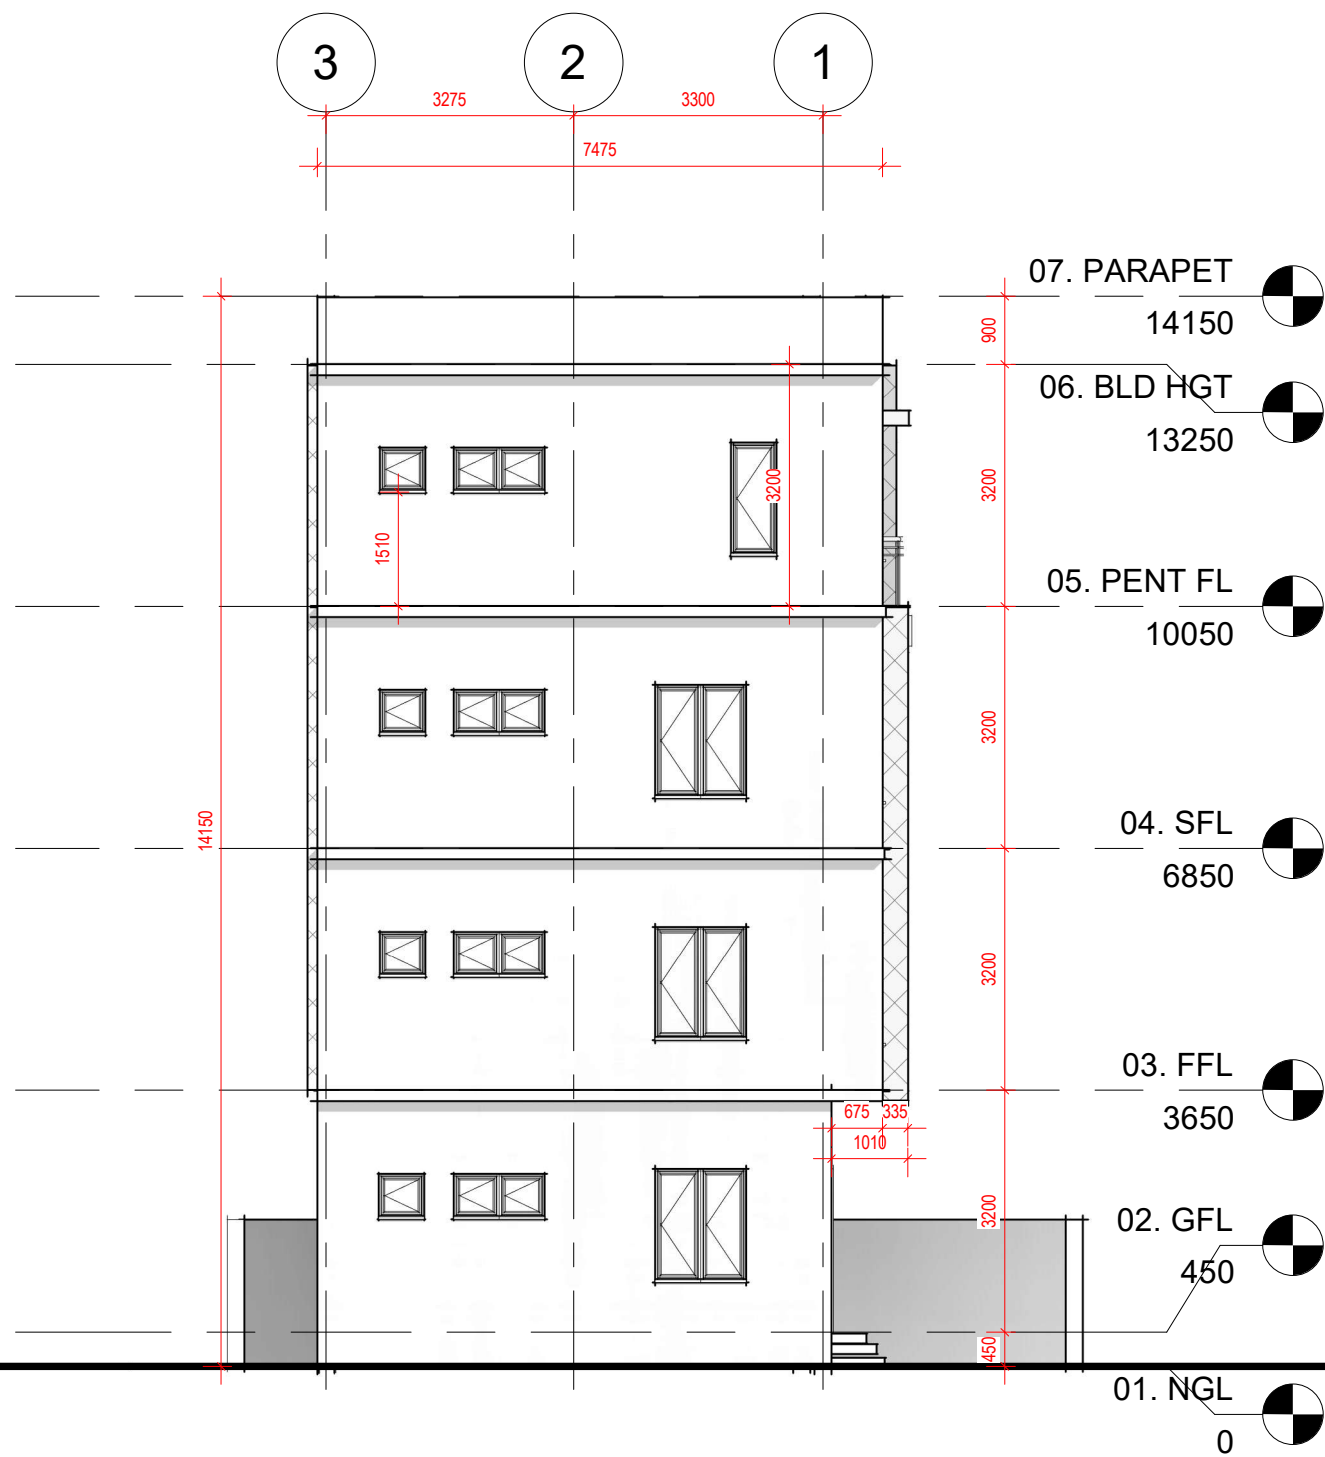

RARE VIEW

NOTES:

- * All dimensions are in millimeters
- * All dimensions are to be verified on site
- * No dimension to be scaled from drawing
- * Architect to be notified of any discrepancy/changes & he alone will decide on the final instruction

CLIENT:

FROST

PROJECT NAME & ADDRESS:

PROPOSED COMMERCIAL DEVELOPMENT
AT CALL PACK, TRADE FAIR ,LAGOS , NIGERIA

DRAWING TITLE:

ELEVATION

DATE: JULY,2022

SCALE:

1 : 100

SHEET NO:

A114

FIRM NAME & ADDRESS:





PELICAN CONSTRUCTION

DRAWN BY:

OLALEKE

CHECKED BY:

ARC. OLALEKE

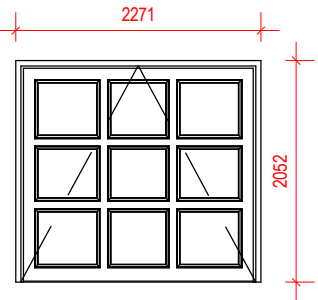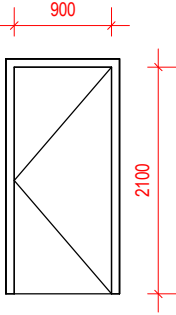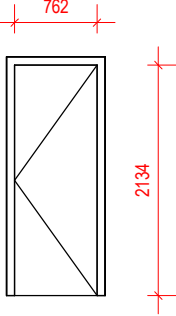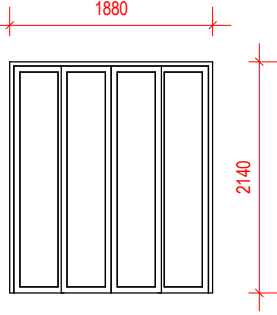						APPROVAL	
TYPE	DOOR DESCRIPTION / SIZE	DOOR DESCRIPTION / SIZE	LOCATION	QUANTITY	REMARKS		
D1	2270mmx2100mm Solid Core Alluminium garrage Security Door. 44mm Thick Finish: Akala Plywood Matt Polyurethane Laquered Finish. Frame: Full Rebated Frame. Architrave: Moulded Architrave 90x15mm Thick.		MAIN ENTRANCE	1	The Section must be of acceptable standard.		
D2	900mm x 2100mm Solid Core Timber Single Leaf Panel Security Door. 44mm Thick Finish: Akala Plywood Matt Polyurethane Laquered Finish. Frame: Full Rebated Frame. Architrave: Moulded Architrave 90x15mm Thick.		CIRCULATION AREA OFFICE SPACE STORE	10	The Section must be of acceptable standard.		
D3	750mm x 2100mm Solid Core Aluminuim Double Sliding Security Door. 44mm Thick Finish: Akala Plywood Matt Polyurethane Laquered Finish. Frame: Full Rebated Frame. Architrave: Moulded Architrave 90x15mm Thick.		W.C	4	The Section must be of acceptable standard.		
D4	1800mm x 2100mm SOLID CORE SLIDDING GLASS PANEL DOOR. 44mm Thick Finish: Akala Plywood Matt Polyurethane Laquered Finish. Frame: Full Rebated Frame. Architrave: Moulded Architrave 90x15mm Thick.		BOSS OFFICE	1	The Section must be of acceptable standard.		

NOTES:

* All dimensions are in millimeters
 * All dimensions are to be verified on site
 * No dimension to be scaled from drawing
 * Architect to be notified of any discrepancy/changes & he alone will decide on the final instruction

CLIENT:

FROST

PROJECT NAME & ADDRESS.

PROPOSED COMMERCIAL DEVELOPMENT
AT CALL PACK, TRADE FAIR ,LAGOS , NIGERIA

DRAWING TITLE:

DOOR SCHEDULE

DATE:

JULY,2022

SCALE:

1 : 70

SHEET NO:

A115

FIRM NAME & ADDRESS:




PELICAN CONSTRUCTION

DRAWN BY:

OLALEKE

CHECKED BY:

ARC. OLALEKE

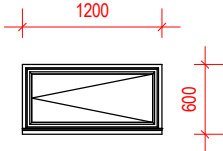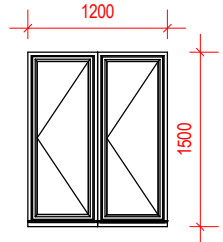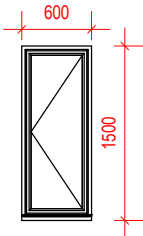TYPE	WINDOW DESCRIPTION / SIZE	WINDOW DESCRIPTION / SIZE	LOCATION	QUANTITY	REMARKS
W1	1200mm x 600mm , anodised aluminium casement window with insect screen and tinted glazing		W.C	4	The Section must be of acceptable standard.
W2	1200mm x 1800mm 3 panel, anodised aluminium casement window with insect screen and tinted glazing		CIRCULATION AREA STORE OFFICE SPACE	10	The Section must be of acceptable standard.
W3	600mm x 1800mm 1 panel, anodised aluminium casement window with insect screen and tinted glazing		STAIR AREA	3	The Section must be of acceptable standard.

NOTES:

- * All dimensions are in millimeters
- * All dimensions are to be verified on site
- * No dimension to be scaled from drawing
- * Architect to be notified of any discrepancy/changes & he alone will decide on the final instruction

CLIENT:

FROST

PROJECT NAME & ADDRESS.

PROPOSED COMMERCIAL DEVELOPMENT
AT CALL PACK, TRADE FAIR ,LAGOS , NIGERIA

DRAWING TITLE:

WINDOW SCHEDULE

DATE: JULY,2022

SCALE:

1 : 65

SHEET NO:

A116

FIRM NAME & ADDRESS:


PELICAN CONSTRUCTION

DRAWN BY:


OLALEKE

CHECKED BY:


ARC. OLALEKE

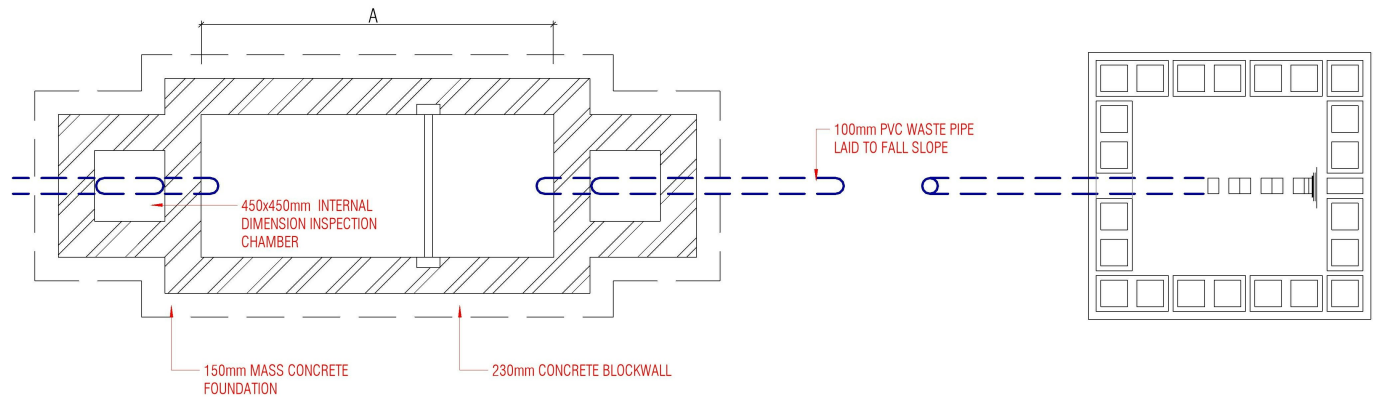

SEPTIC TANK / SOAK AWAY FLOOR PLAN
1 : 50

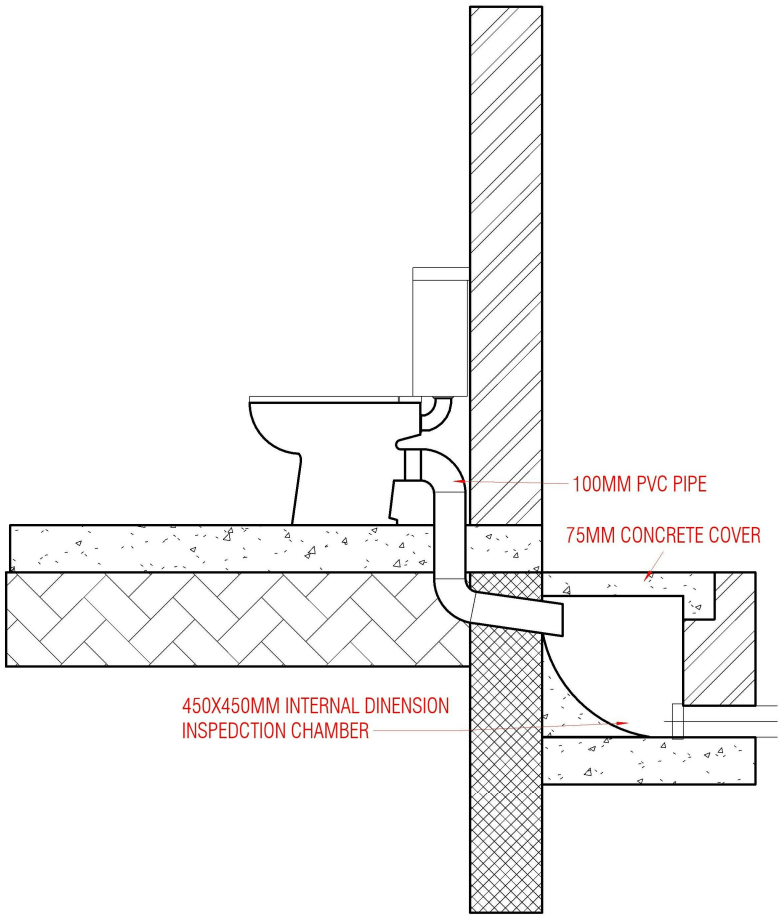


WC DETAIL
1 : 25

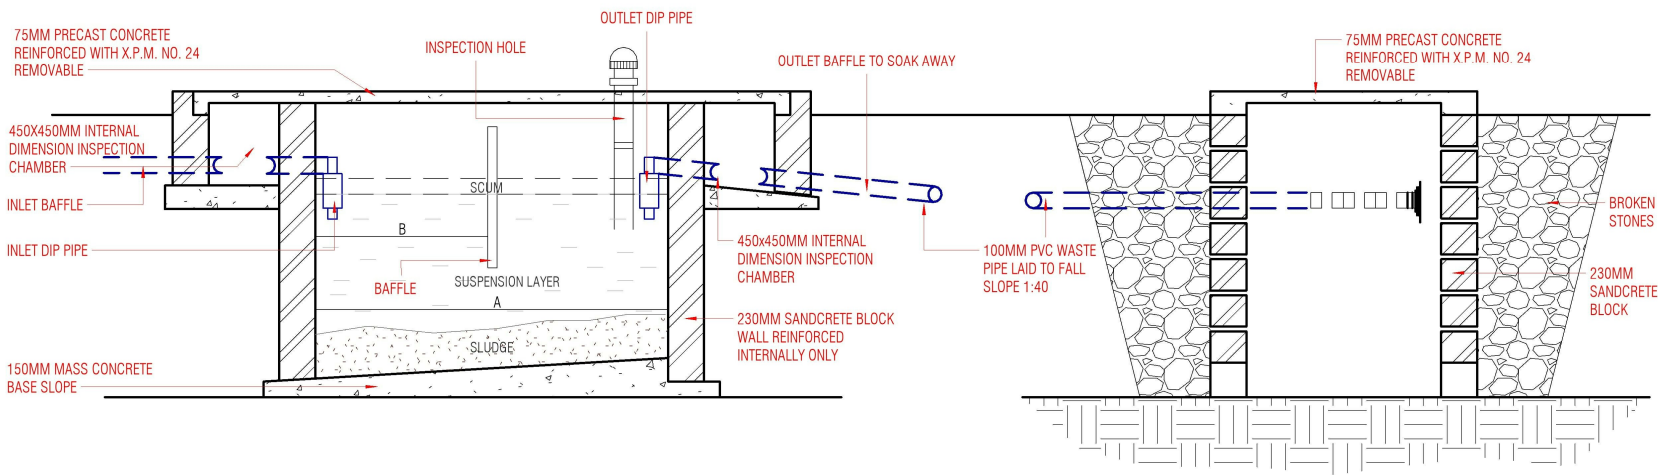


SEPTIC TANK / SOAK AWAY SECTION 1
1 : 50

1	2				3	4	5	6	7	8	9
	DIMENSIONS				CAPACITY CUB. FIT	NO OF USERS		EQUIV. OF G.D.P.	BALANCE OF TRENCH		
	A	B	C	D		ALL WASTE	SOLID WASTE ONLY		2G/OFT	4G/OFT	6G/OFT
I	1600	1600	1600	1600	40	10	10	250	3750MM	2700MM	2175MM
II	2250	2250	2250	2250	52.5	13	15	325	4350MM	3075MM	2550MM
III	2250	2250	2250	2250	60	15	20	375	4950MM	3700MM	2700MM
IV	2500	2500	2500	2500	75	18	30	470			
V	3000	3000	3000	3000	100	25	40	625			
VI	3600	3600	3600	3600	200	30	100				

SEPTIC TANK / SOAK AWAY SCHEDULE
1 : 50

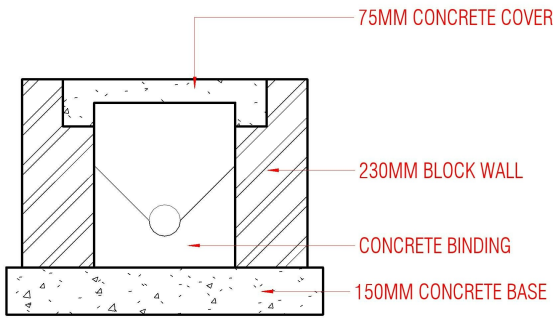

SECTION 2
1 : 25

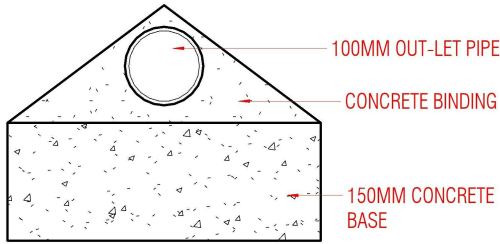

SECTION 3
1 : 10

NOTES:

- * All dimensions are in millimeters
- * All dimensions are to be verified on site
- * No dimension to be scaled from drawing
- * Architect to be notified of any discrepancy/changes & he alone will decide on the final instruction

CLIENT:

FROST

PROJECT NAME & ADDRESS.

PROPOSED COMMERCIAL DEVELOPMENT
AT CALL PACK, TRADE FAIR ,LAGOS , NIGERIA

DRAWING TITLE:

SEPTIC TANK &
SOAK-AWAY

DATE: JULY,2022

SCALE:

SHEET NO:

A117

FIRM NAME & ADDRESS:

PELICAN CONSTRUCTION

DRAWN BY:

OLALEKE

CHECKED BY:

ARC. OLALEKE



NOTES:

- * All dimensions are in millimeters
- * All dimensions are to be verified on site
- * No dimension to be scaled from drawing
- * Architect to be notified of any discrepancy/changes & he alone will decide on the final instruction

CLIENT:

FROST

PROJECT NAME & ADDRESS.

PROPOSED COMMERCIAL DEVELOPMENT

AT CALL PACK, TRADE FAIR ,LAGOS , NIGERIA

DRAWING TITLE:

3D VIEW

DATE: JULY,2022

SCALE:

SHEET NO:

A118

FIRM NAME & ADDRESS:

PELICAN CONSTRUCTION

DRAWN BY:

OLALEKE

CHECKED BY:

ARC. OLALEKE